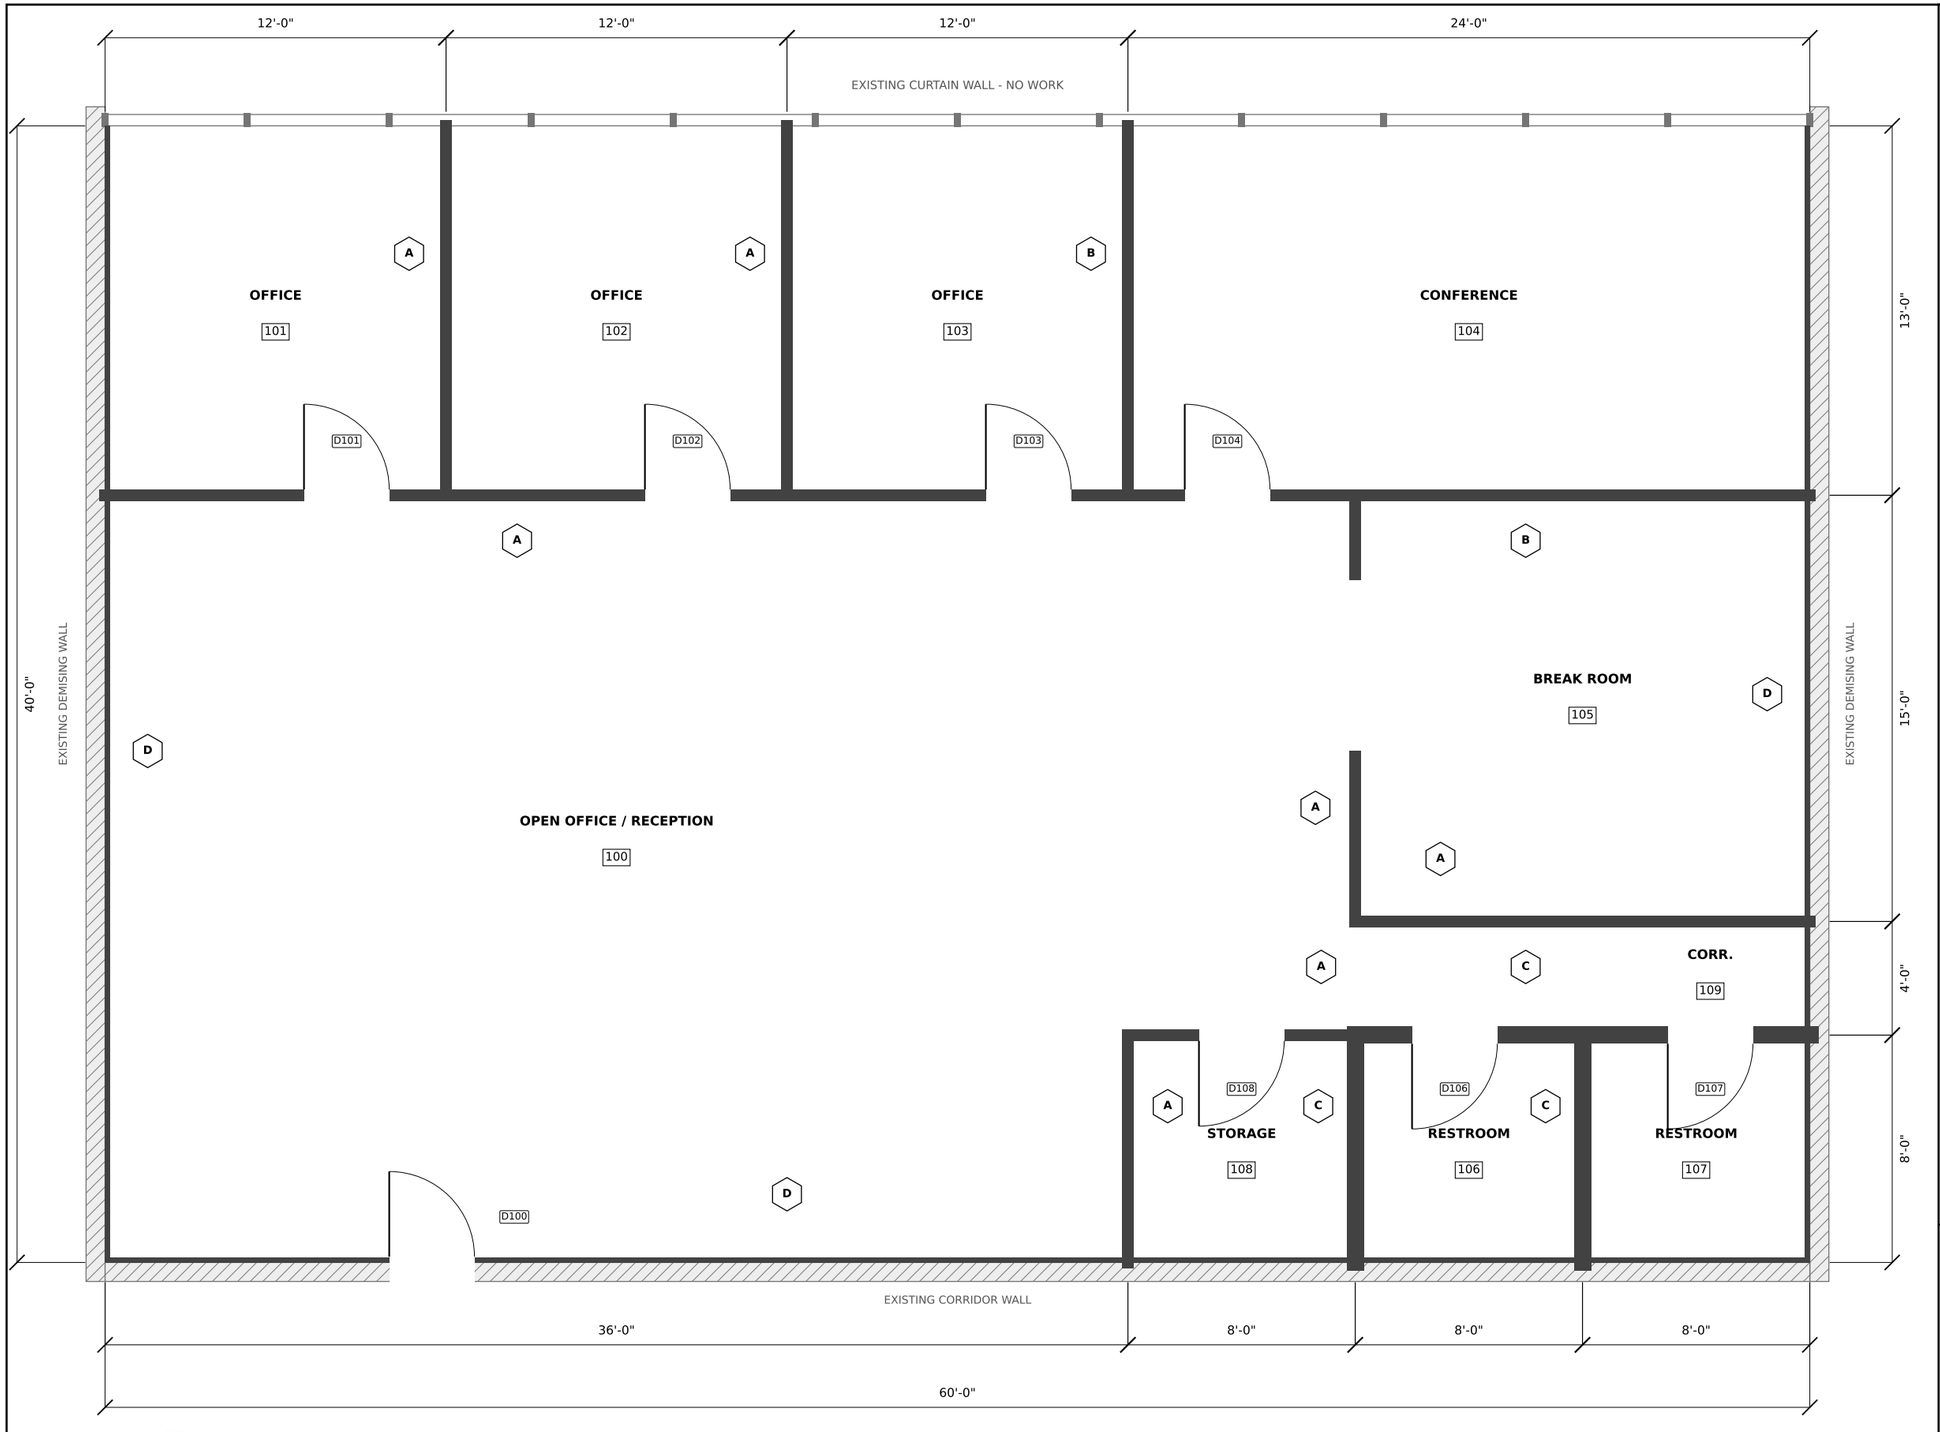


1 A-101

PARTITION PLAN

SCALE: 3/16" = 1'-0"

PARTITION TYPES

A — 3-5/8" 20 GA EQ STUDS @ 16" O.C., 1 LAYER 5/8" TYPE X GWB EACH SIDE
TO 6" ABOVE CEILING (9'-6" AFF)

B — 3-5/8" 20 GA EQ STUDS @ 16" O.C., 1 LAYER 5/8" TYPE X GWB EACH SIDE, 3-1/2" SOUND BATTS
FULL HEIGHT TO DECK (13'-0" AFF)

C — 6" 20 GA EQ STUDS @ 16" O.C., 1 LAYER 5/8" MOISTURE-RESISTANT GWB EACH SIDE, 3-1/2" SOUND BATTS
FULL HEIGHT TO DECK (13'-0" AFF)

D — 1-5/8" 25 GA STUDS @ 24" O.C. FURRING AT EXISTING WALL, 1 LAYER 5/8" TYPE X GWB SUITE SIDE
FULL HEIGHT TO DECK (13'-0" AFF)

DOOR / OPENING SCHEDULE

D101-D104, D106-D108	3'-0" x 7'-0" WOOD DOOR, HM FRAME
CO1	6'-0" x 7'-0" CASED OPENING, GWB RETURNS
D100	EXISTING ENTRY DOOR TO REMAIN


GENERAL NOTES

1. Dimensions to partition centerlines U.N.O.
2. Ceiling height 9'-0" AFF U.N.O., see A-201.
3. Underside of deck 13'-0" AFF.
4. Restrooms 106 / 107: GWB ceiling at 8'-0" AFF.
5. Existing walls and curtain wall: no work except Type D furring on suite side.
6. Portfolio sample - not for construction.

PROJECT	**SUITE 210 - TENANT FIT-OUT** **PORTFOLIO SAMPLE**
SHEET	**PARTITION PLAN**
DRAWN	S. GRISHUTOV (SAMPLE SET)
SCALE	3/16" = 1'-0" @ 11x17
DATE	NOV 2026

NOT FOR CONSTRUCTION

A-101

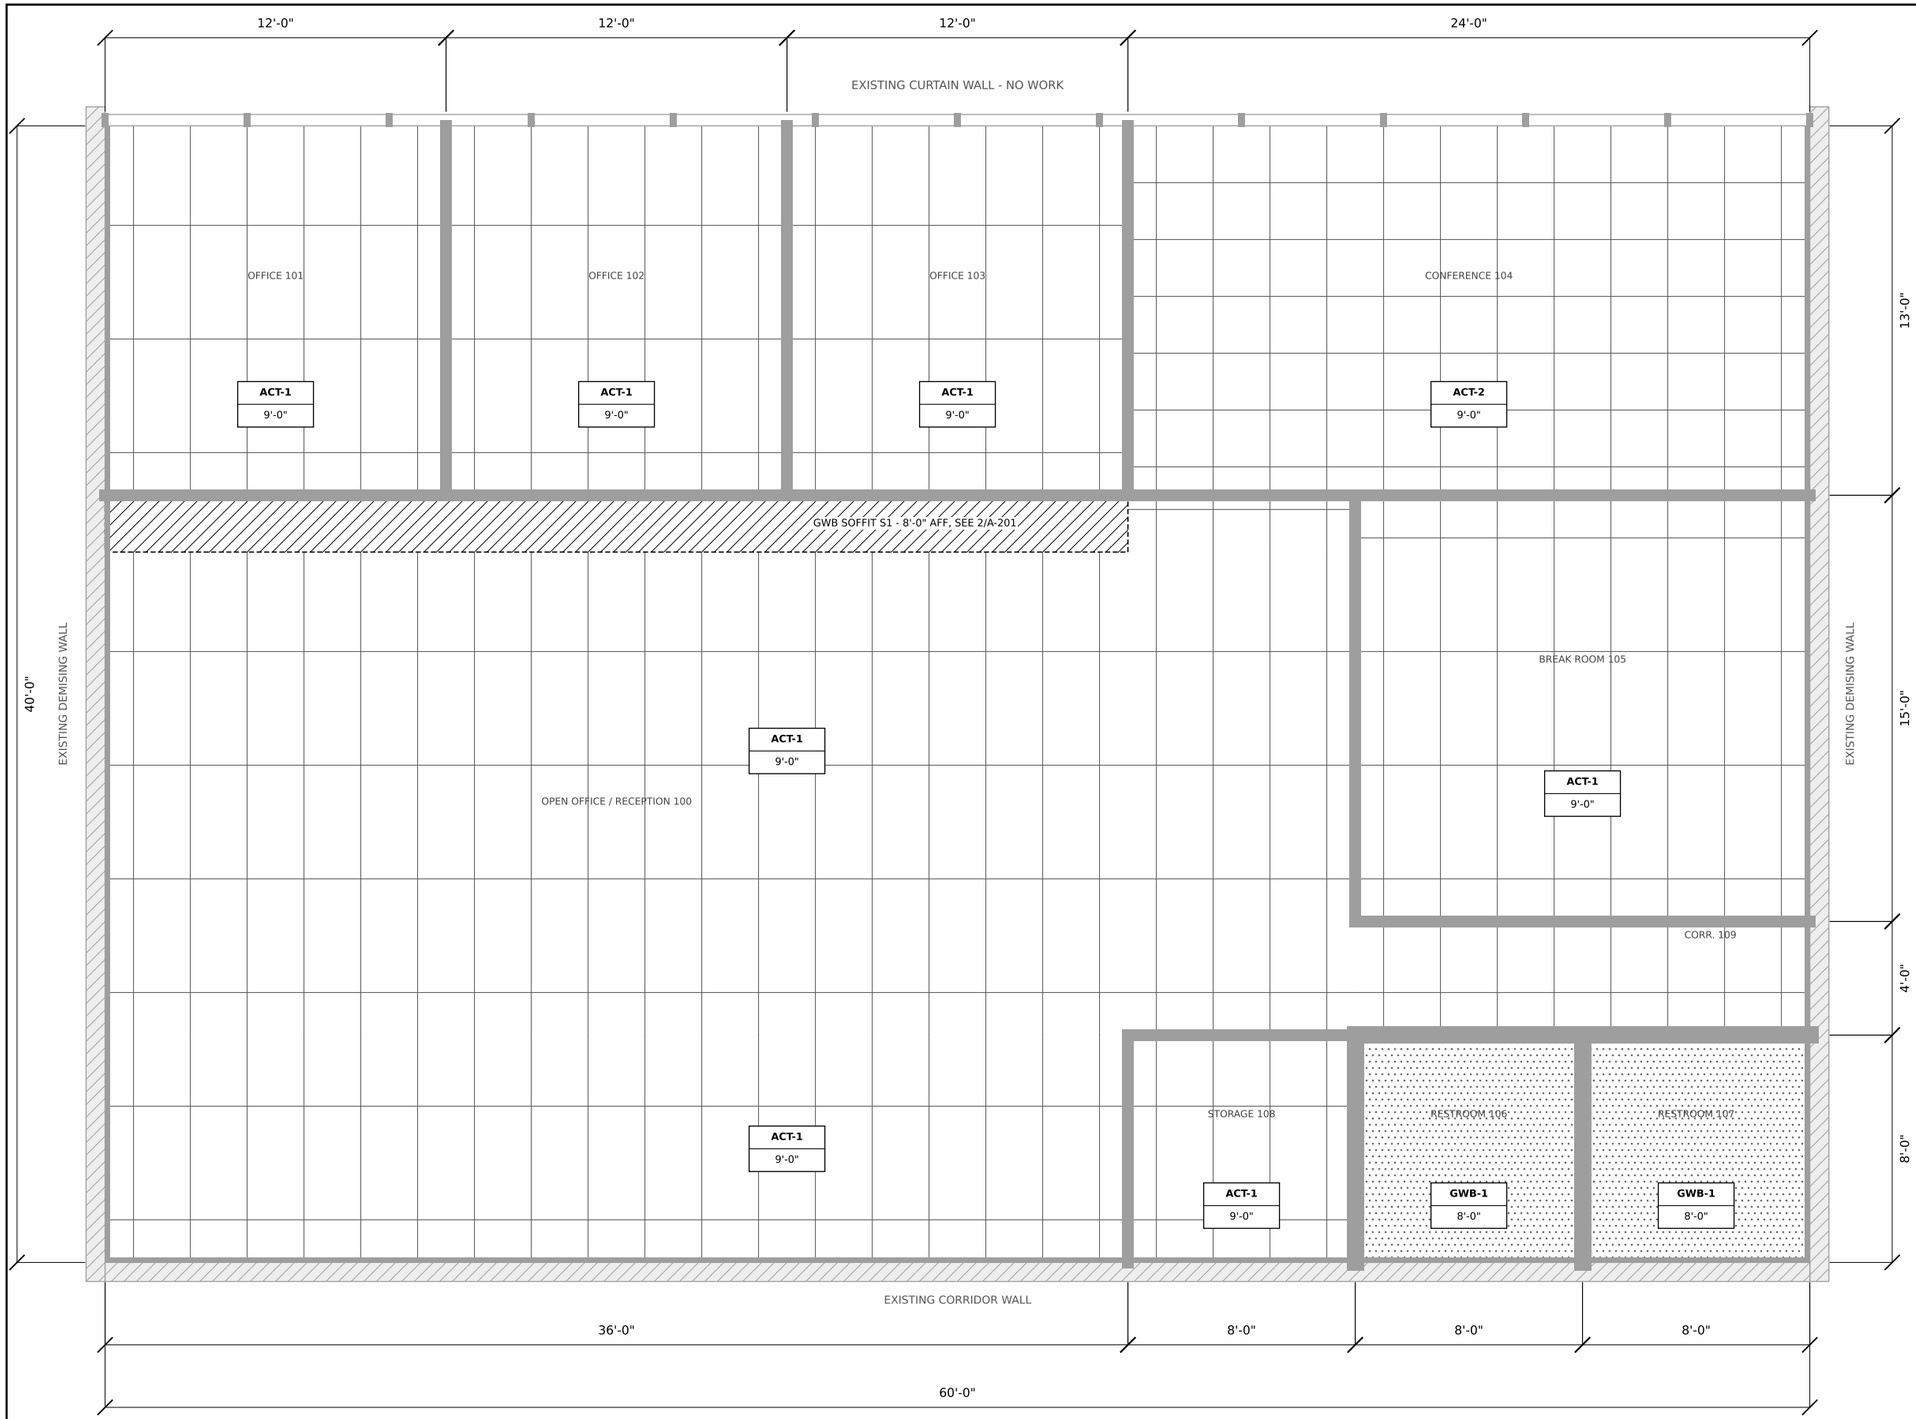

1 A-201

REFLECTED CEILING PLAN

SCALE: 3/16" = 1'-0"

CEILING LEGEND

ACT-1
2' X 4' ACOUSTIC CEILING TILE ON 15/16" EXPOSED GRID


ACT-2
2' X 2' ACOUSTIC CEILING TILE ON 15/16" EXPOSED GRID

GWB-1
5/8" MOISTURE-RESISTANT GWB ON DRYWALL SUSPENSION GRID

GWB-2
5/8" TYPE X GWB SOFFIT ON DRYWALL SUSPENSION GRID

RCP NOTES

1. Ceiling heights are above finished floor (AFF).
2. Start grid per tags, balance borders in rooms.
3. Restroom ceilings: moisture-resistant GWB, paint.
4. Lights, diffusers and sprinklers not shown.
5. Portfolio sample - not for construction.

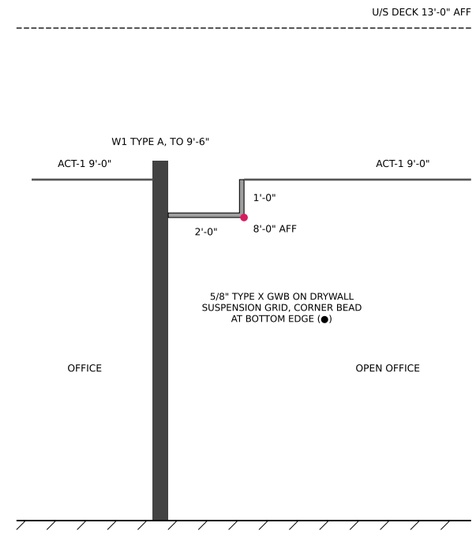

2 A-201

SOFFIT S1 SECTION

SCALE: 1/4" = 1'-0"

PROJECT	**SUITE 210 - TENANT FIT-OUT**
	PORTFOLIO SAMPLE
SHEET	**REFLECTED CEILING PLAN**
DRAWN	S. GRISHUTOV (SAMPLE SET)
SCALE	3/16" = 1'-0" @ 11x17
DATE	NOV 2026

NOT FOR CONSTRUCTION

A-201