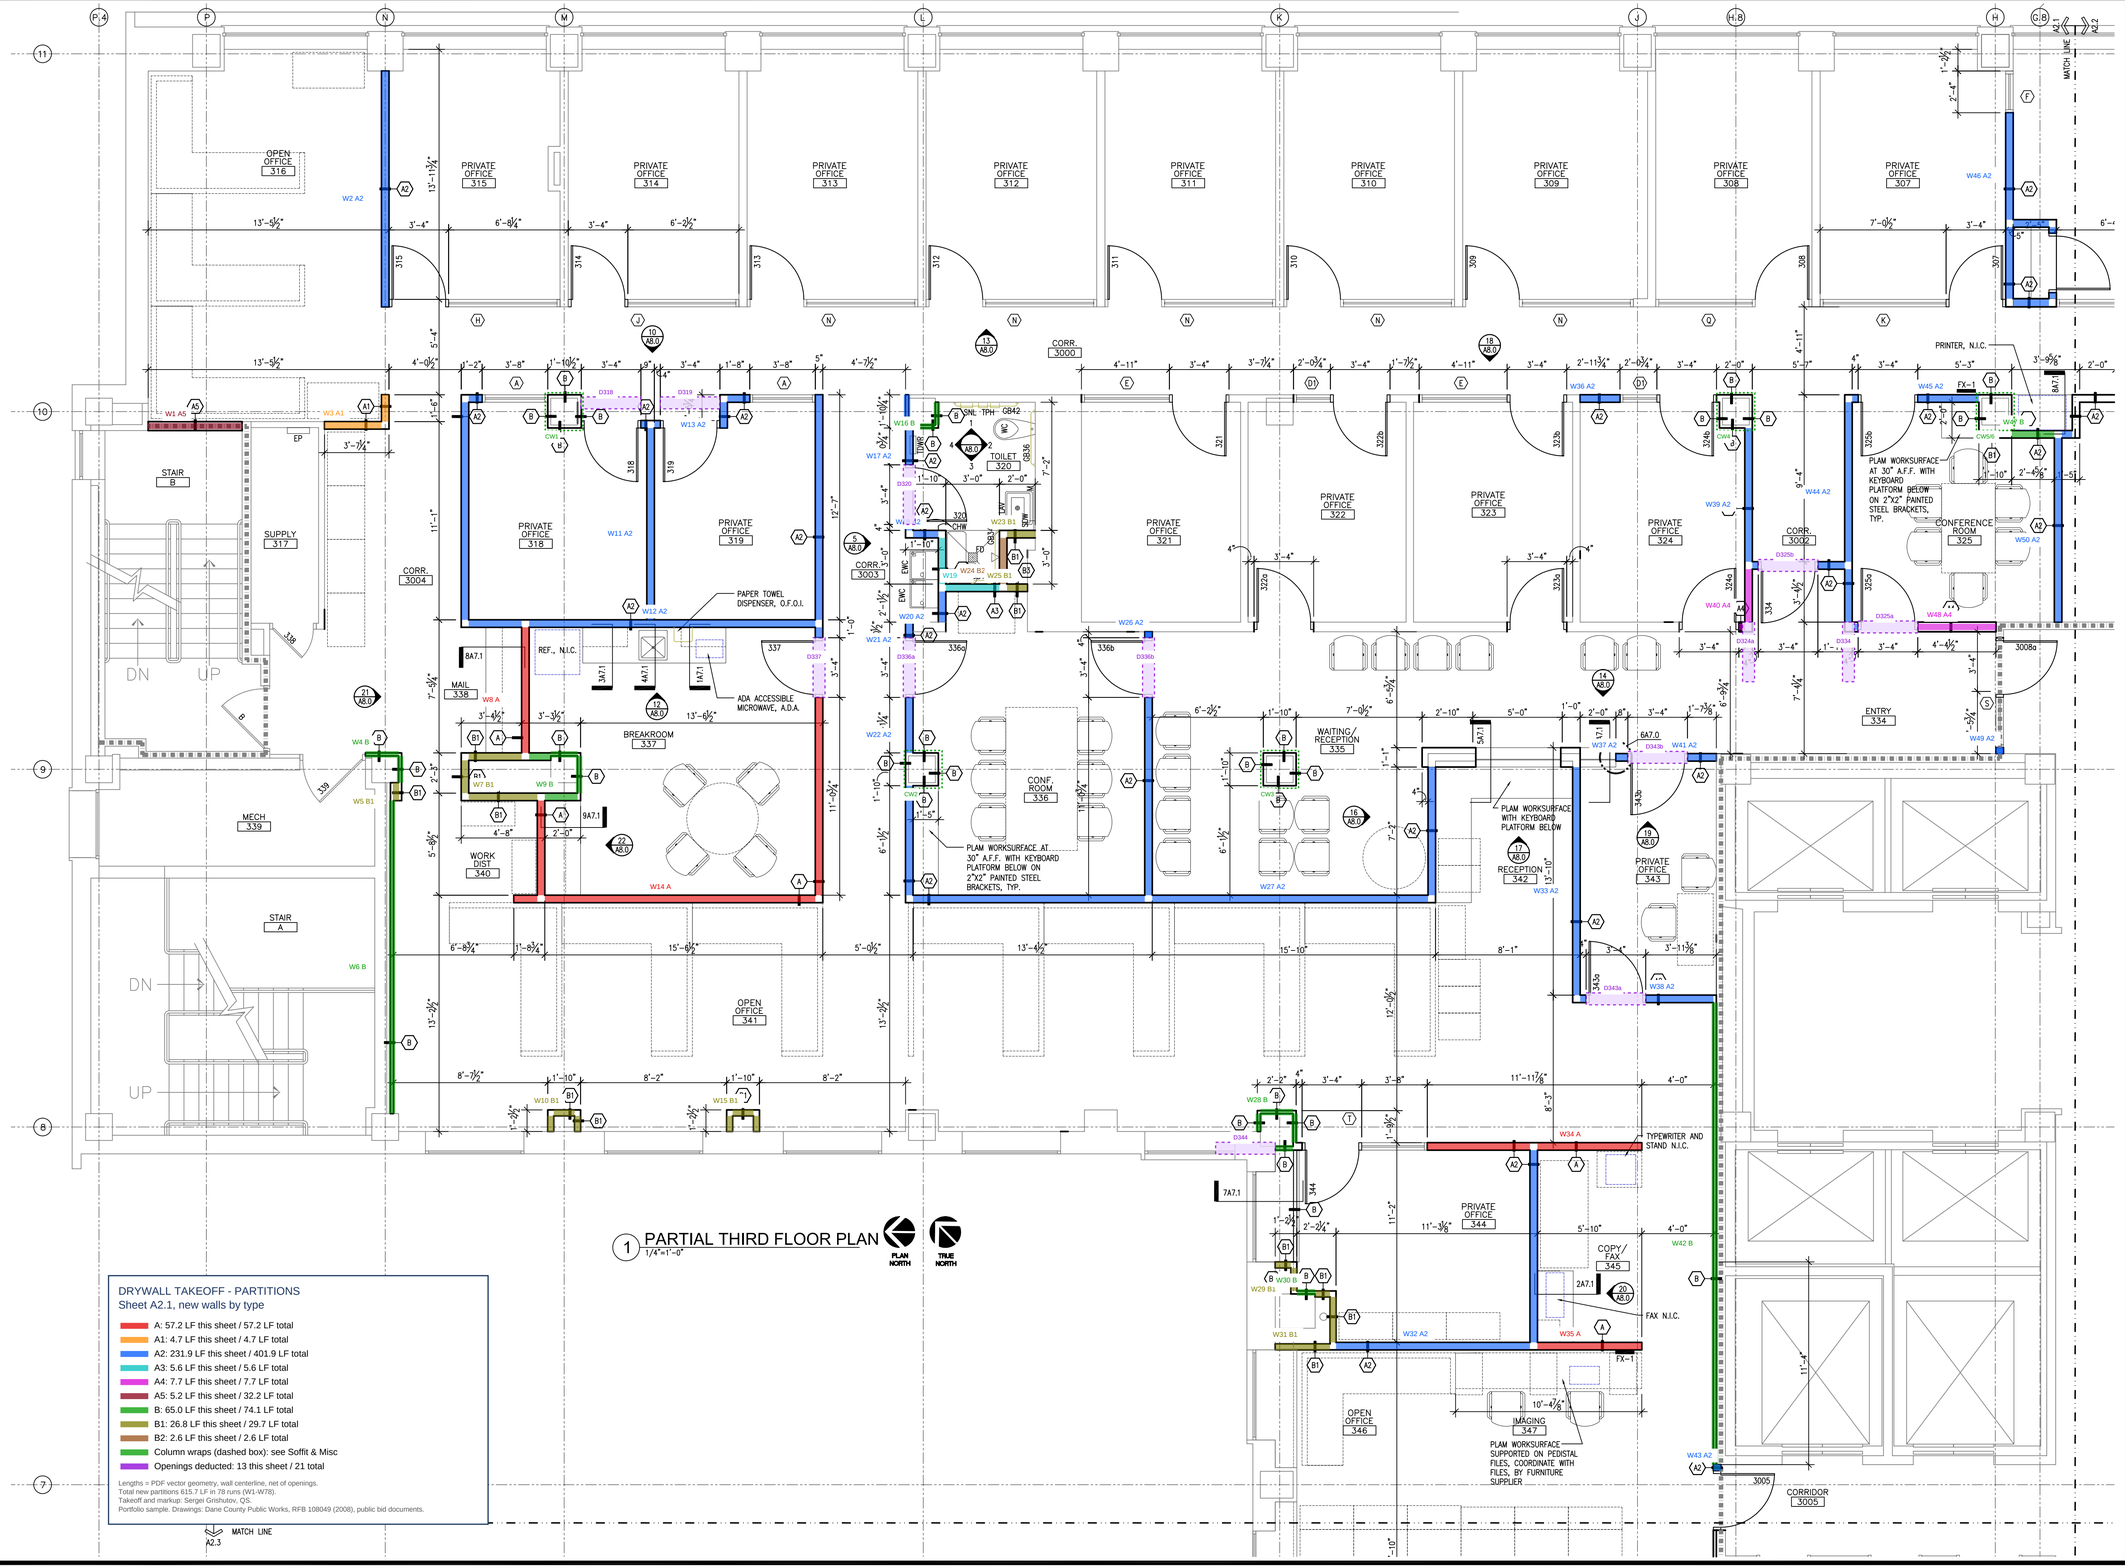


1 PARTIAL THIRD FLOOR PLAN
1/4"=1'-0"

PLAN NORTH / TRUE NORTH

DRYWALL TAKEOFF - PARTITIONS
Sheet A2.1, new walls by type

- A: 57.2 LF this sheet / 57.2 LF total
- A1: 4.7 LF this sheet / 4.7 LF total
- A2: 231.9 LF this sheet / 401.9 LF total
- A3: 5.6 LF this sheet / 5.6 LF total
- A4: 7.7 LF this sheet / 7.7 LF total
- A5: 5.2 LF this sheet / 32.2 LF total
- B: 65.0 LF this sheet / 74.1 LF total
- B1: 26.8 LF this sheet / 29.7 LF total
- B2: 2.6 LF this sheet / 2.6 LF total
- Column wraps (dashed box): see Soffit & Misc
- Openings deducted: 13 this sheet / 21 total

Lengths = PDF vector geometry, wall centerline, net of openings.
Total new partitions 615.7 LF in 78 runs (W1-W78).
Takeoff and markup: Sergei Grishutov, QS.
Portfolio sample. Drawings: Dane County Public Works, RFB 108049 (2008), public bid documents.

DORSCHNER ASSOCIATES
Architecture
Planning
Dorschner|Associates, Inc.
849 E. Washington Ave., Ste 112
Madison, Wisconsin 53703


ISSUED

PROJECT
TENANT IMPROVEMENTS
THIRD FLOOR
CITY–COUNTY BUILDING
210 MARTIN LUTHER KING, JR. BLVD., MADISON, WI

DRAWING
ENLARGED PARTIAL THIRD FLOOR PLAN

DATE
03.10.08

A2.1

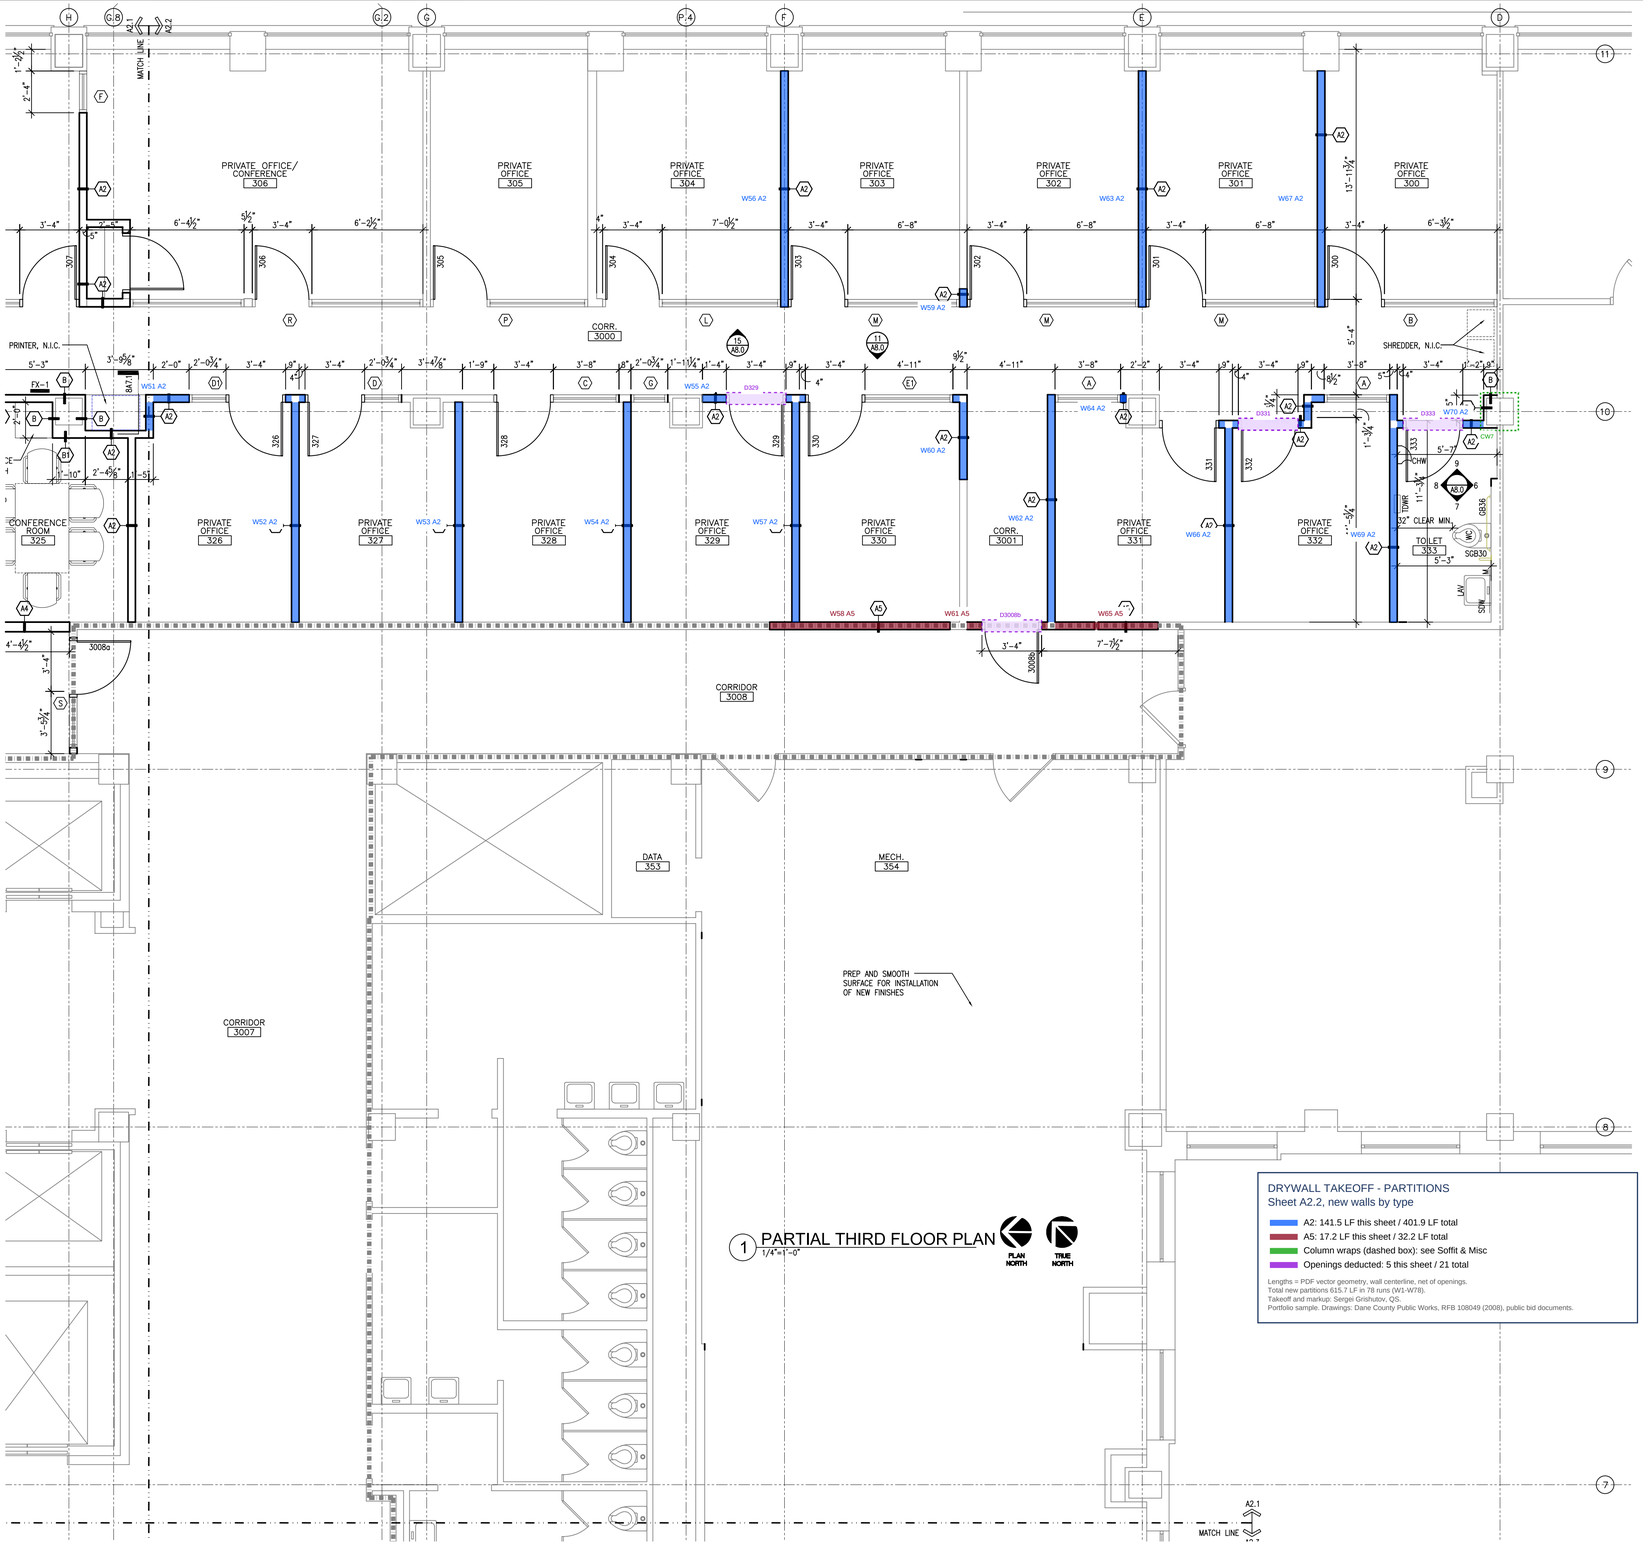

1 PARTIAL THIRD FLOOR PLAN
1/4"=1'-0"

PLAN NORTH

TRUE NORTH

DRYWALL TAKEOFF - PARTITIONS
Sheet A2.2, new walls by type

- A2: 141.5 LF this sheet / 401.9 LF total
- A5: 17.2 LF this sheet / 32.2 LF total
- Column wraps (dashed box): see Soffit & Misc
- Openings deducted: 5 this sheet / 21 total

Lengths = PDF vector geometry, wall centerline, net of openings.
Total new partitions 615.7 LF in 78 runs (W1-W78).
Takeoff and markup: Sergei Grishutov, QS.
Portfolio sample. Drawings: Dane County Public Works, RFB 108049 (2008), public bid documents.

DORSCHNER ASSOCIATES
Architecture
Planning

Dorschner|Associates, Inc.
849 E. Washington Ave., Ste 112
Madison, Wisconsin 53703

ISSUED

PROJECT
TENANT IMPROVEMENTS
THIRD FLOOR
CITY–COUNTY BUILDING
210 MARTIN LUTHER KING,
JR. BLVD., MADISON, WI

DRAWING
ENLARGED PARTIAL THIRD
FLOOR PLAN

DATE
03.10.08

A2.2

DRYWALL TAKEOFF - PARTITIONS
Sheet A2.3, new walls by type

- A2: 28.5 LF this sheet / 401.9 LF total
- A5: 9.7 LF this sheet / 32.2 LF total
- B: 9.1 LF this sheet / 74.1 LF total
- B1: 2.9 LF this sheet / 29.7 LF total
- Openings deducted: 3 this sheet / 21 total

Lengths = PDF vector geometry, wall centerline, net of openings.
Total new partitions 615.7 LF in 78 runs (W1-W78).
Takeoff and markup: Sergei Grishutov, QS.
Portfolio sample. Drawings: Dane County Public Works, RFB 108049 (2008), public bid documents.

A2.1

7.2

6

5

3005

W78 B

STAIR C

DN

UP

17'-10"

W71 B1

3'-4¼"

1'-11"

FILE AREA 348

PLAM WORKSURFACE SUPPORTED ON PEDISTAL FILES, COORDINATE WITH FILES, BY FURNITURE SUPPLIER

PATCH TO MATCH EXISTING ADJACENT WITH GWB, PROVIDE EDGE BEAD AT CORNER

FX-1

349

CONFERENCE ROOM 349

51'-3"

10'-5⅜"

3'-4"

4"

W72 A2

D3006 76 A5

W75 A2

3006

9'-1³⁄₈"

1'-1½"

W74 A5

CORRIDOR 3006

PRIVATE OFFICE 350

1'-9⅞"

FX-1

D350

2'-4"

350

W73 A2

D351

351

352

10'-0⅞"

3'-4"

11'-4¼"

10'-5⅞"

W77 A2

PRIVATE OFFICE 351

FILE AREA 352

1 THIRD FLOOR PLAN
1/4"=1'-0"

PLAN NORTH

TRUE NORTH

DORSCHNER ASSOCIATES
Architecture
Planning

Dorschner|Associates, Inc.
849 E. Washington Ave., Ste 112
Madison, Wisconsin 53703


ISSUED

PROJECT
TENANT IMPROVEMENTS
THIRD FLOOR
CITY-COUNTY BUILDING
210 MARTIN LUTHER KING,
JR. BLVD., MADISON, WI

DRAWING
ENLARGED PARTIAL THIRD
FLOOR PLAN

DATE
03.10.08

A2.3

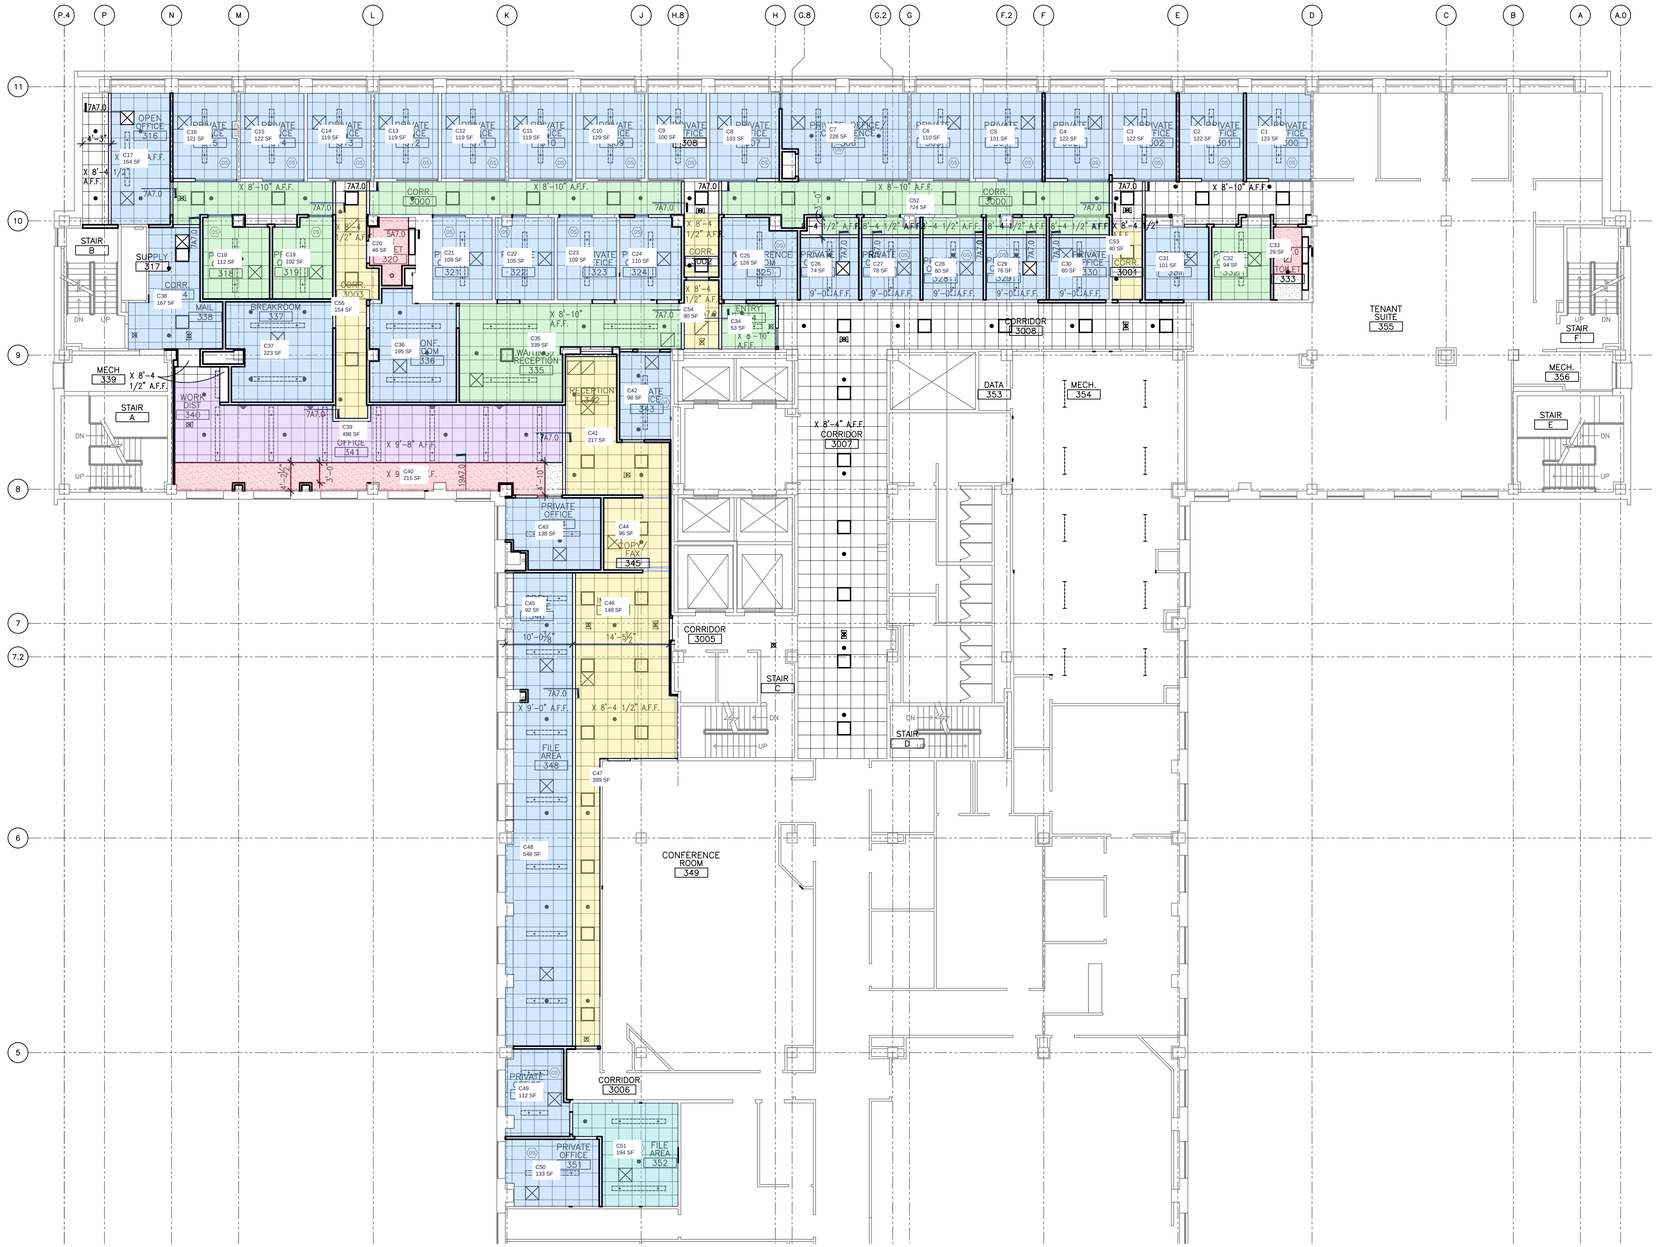

1 THIRD FLOOR REFLECTED CEILING PLAN
3/32"=1'-0"

PLAN NORTH

TRUE NORTH

REFLECTED CEILING PLAN SYMBOLS

- GYPSUM WALL BOARD
- 2'X2' ACOUSTICAL CEILING TILE
- 2'X2' FLUORESCENT LIGHT FIXTURE, SEE ELECTRICAL
- 1'X8' LINEAR FLUORESCENT INDIRECT PENDANT FIXTURE. SEE ELECTRICAL
- 1'X4' LINEAR FLUORESCENT INDIRECT PENDANT FIXTURE. SEE ELECTRICAL
- 1'X4' FLUORESCENT INDIRECT SCONCE FIXTURE. SEE ELECTRICAL
- 1'X4' FLUORESCENT. SEE ELECTRICAL
- EXIT LIGHT, ARROW INDICATES DIRECTION PLACE CENTER OF 2x2' TILE
- HVAC SUPPLY DIFFUSER
- HVAC EXHAUST/TRANSFER DIFFUSER
- HVAC EXHAUST DIFFUSER
- OCCUPANCY SENSOR
- SPRINKLER HEAD

REFLECTED CEILING PLAN GENERAL NOTES

1. FIELD VERIFY ALL CONDITIONS, NOTIFY ARCHITECT OF ANY DISCREPANCY.
2. SEE MECHANICAL FOR COORDINATION OF EQUIPMENT LOCATIONS.
3. SEE ELECTRICAL FOR FIXTURE TYPES.
4. CENTER ALL FIXTURES IN ACT.
5. SEE ROOM FINISH SCHEDULE FOR MORE INFORMATION.
6. PREFERRED SPRINKLER HEAD LOCATIONS INDICATED. INSTALL PER NFPA 13, SEE SPECIFICATION SECTION C15010.

DRYWALL TAKEOFF - CEILINGS

Sheet A3.0, by type and height

- ACT @ 9'-8": 498.3 SF
- ACT @ 9'-2": 193.6 SF
- ACT @ 9'-0": 4,955.3 SF
- ACT @ 8'-10": 1,423.2 SF
- ACT @ 8'-4 1/2": 1,144.6 SF
- GWB @ 9'-0": 215.4 SF
- GWB @ 8'-0": 74.4 SF

Total new ceilings 8,504.8 SF in 55 areas (C1-C55).
Heights: Room Finish Schedule A9.0; areas from A3.0 vector linework.
Existing ceilings (317, 339, 349, 3005-3009) not marked.
Takeoff and markup: Sergei Grishutov, QS.
Portfolio sample. Drawings: Dane County Public Works, RFB 108049 (2008), public bid documents.

DORSCHNER ASSOCIATES
Architecture
Planning
Dorschner|Associates, Inc.
849 E. Washington Ave., Ste 112
Madison, Wisconsin 53703

ISSUED

PROJECT
TENANT IMPROVEMENTS
THIRD FLOOR
CITY–COUNTY BUILDING
210 MARTIN LUTHER KING, JR. BLVD., MADISON, WI

DRAWING
THIRD FLOOR REFLECTED CEILING PLAN

DATE
03.10.08

A3.0